


Claint Sl No	Purchaser Name	Grand Total Dec	Total Kata	BHK	SQFT	Parking
1	Jasimuddin Mandal	2.6061	1.58		1340	1
2.a	Maidul Islam	1.0350	0.63	2BHK	720	-
2.b	Sabnam Mustari	1.0350	0.63			
3	Sekh Alauddin	1.4125	0.86	2BHK	720	1
4.a	Tabassum Haque	0.4350	0.26	3BHK	1340	1
4.b	Musrail Rahaman	0.9561	0.58			
5	Monira Akhter Banu	2.8850	1.75	3BHK	1260	1
6	Imran Ali	1.6500	1.00	2BHK	720	-
7	Aminur Rahaman	1.6500	1.00	2BHK	720	1
8	Adil Faiz	2.0625	1.25	2BHK	900	-
9	Regina Parveen	2.0625	1.25	2BHK	900	-
10	Ahmad Raza	2.0625	1.25	2BHK	900	-
11	Shabnam Mostari	2.0625	1.25	2BHK	900	-
12.a	Shamsul Haque	0.8250	0.50	2BHK	720	-
12.b	Razia Haque	0.8250	0.50			
13.a	Mohammed Rafat sayeed	0.8250	0.50	2BHK	720	-
13.b	Tazeen Shadan	0.8250	0.50			
14	Jalaluddin Molla	2.8250	1.71	3BHK	1340	1
15	Hossain Md Soukat Ali	1.5250	0.92	3BHK	1080	-
	Sonali Parvin	0.2250	0.14			
	Emili Parvin	0.2250	0.14			
16	Mustakin Ahamed	8.8000	5.33	J.V		
17	Rupali Parvin	2.4000	1.45	J.V		
18.a	Bahadur Ali Mondal	1.3250	0.80	3BHK	1080	-
18.b	Rojina Pervin	1.3250	0.80			-
19	Sk Sahim Uddin	1.6525	1.00	2BHK	720	-
	THINK REAL ESTATE	4.0800	2.47			
	THINK REAL ESTATE	4.0900	2.48			
20	MASUMA KHATUN	1.6500	1.00	2BHK	720	-
21	RAJINA PRAVIN	1.6500	1.00	2BHK	720	-
22	SABINA KHATUN	2.0625	1.25	3BHK	900	-
23	UNJERA BANU	2.0625	1.25	3BHK	900	-
24.a	SHAMSUL HAQUE	0.8250	0.50	2BHK	720	-
24.b	MALEK HASSAIN	0.8250	0.50			
25	SOHEL AHMED	2.6425	1.60	3BHK	1080	-
	THINK REAL ESTATE	0.8125	0.49			
26	FARHANAZ BEGUM	1.2375	0.75	1BHK	540	-
27	MD MONIRUL ISLAM	1.2375	0.75	1BHK	540	-
	THINK REAL ESTATE	0.8100	0.49			
28.a	MOLLA SARIFUDDIN	0.8250	0.50	2BHK	720	-
28.b	SHAHNAZ PERVEEN	0.8250	0.50			
	THINK REAL ESTATE	0.7500	0.45			
29	MD ZAKARIA	1.6500	1.00	2BHK	720	-
30	AZAD MD SAIFUL HAQUE	1.6500	1.00	3BHK	720	-
	THINK REAL ESTATE	3.2700	1.98			
	THINK REAL ESTATE	0.7500	0.45			
31	YASIN MALICK	0.5000	0.30	2BHK	900	1
32	SAKINA BEGUM	0.5000	0.30	2BHK	720	-
33	ASADUL MALICK	0.5000	0.30	2BHK	720	1
34	ISRAIL MANDAL	0.5000	0.30	2BHK	720	1
35	ARIFUL HAQUE TARAFDAR	0.6000	0.36	2BHK	900	1
36	KH MASUDA KHANAM	1.6500	1.00	2BHK	720	-
		83.4722	50.59	0	29040	10

SITE PLAN OF PART OF R. S. & L. R. DAG NO'S - 3171,3173,3173/3808, 3174,3174/3809 UNDER L. R. KH. NO'S - , AT MOUZA -PATHORGHATA, J. L. NO - 35, R.S. NO -, P.S. - RAJARHAT (PRESENTLY NEWTOWN), DIST -NORTH 24 PARGANAS, UNDER PATHORGHATA GRAM PANCHAYET.

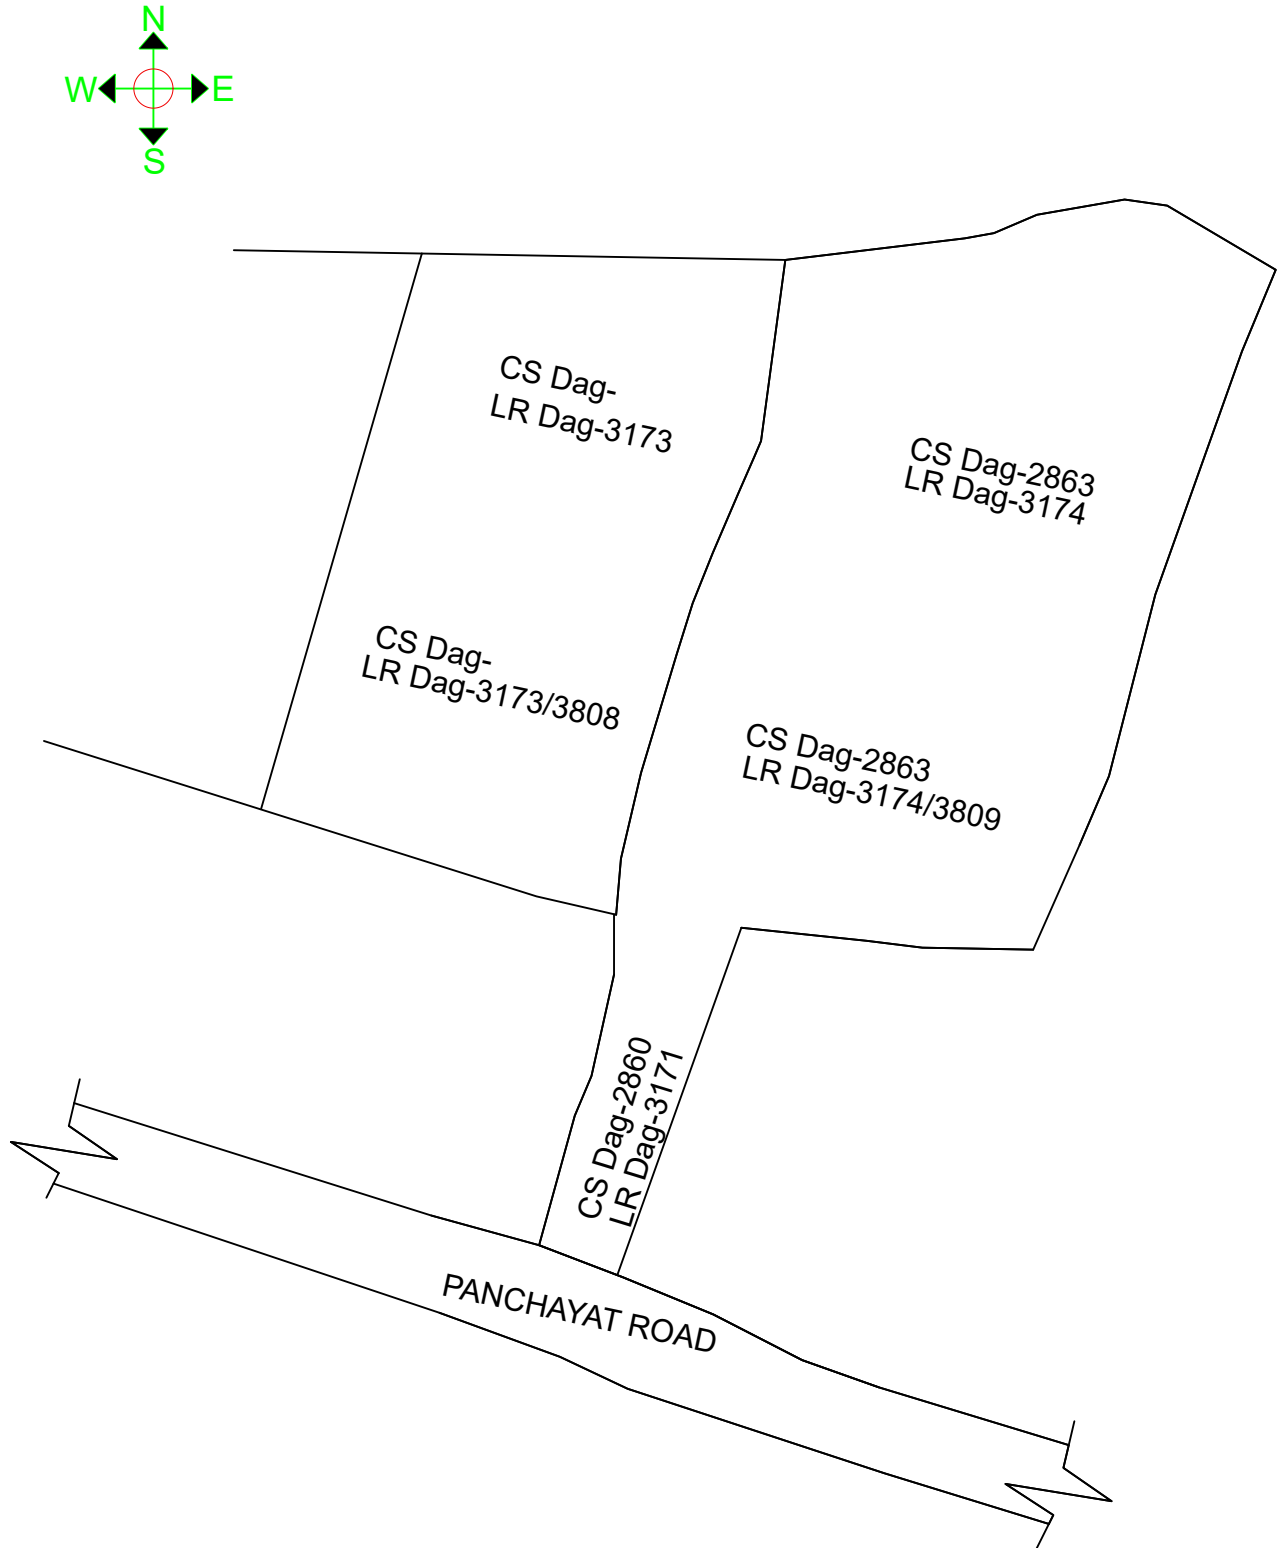

PATHORGHATA				
AS PER LR PORCHA				
SL. NO.	DAG NO.	TOTAL AREA	AREA (DEC)	AREA (KATHA)
1	3171	34	17.00	10.30
2	3173	28	28.00	16.97
3	3173/3808	13	13.00	7.88
4	3174	73	73.00	44.24
5	3174/3809	21	21.00	12.73
TOTAL =		169	152.00	92.12
AS PER DEED				
SL. NO.		DAG NO.	AREA (DEC)	AREA (KATHA)
Deed-2,3	15760/22 15761/22	3171		-
		3174	2.61	1.58
		3174/3809	0.75	0.45
Deed-4	5144/23	3171	4.25	2.58
		3174		-
		3174/3809		-
Deed-6	13206/2023	3171		-
		3174	34.76	21.07
		3174/3809	9.80	5.94
Deed-7	2101/2024	3171		-
		3174	8.69	5.27
		3174/3809	2.45	1.48
Deed-8	13391/24	3171	0.81	0.49
		3174		-
		3174/3809		-
Deed-9	15180/2024	3171		-
		3174	2.61	1.58
		3174/3809	0.75	0.45
Deed-14	14082/25	3171		-
		3174	2.83	1.71
		3174/3809	1.53	0.92
Deed-15	J.V	3171		-
		3174	9.20	5.58
		3174/3809	2.45	1.48
Deed-	/2026			-
				-
				-
Deed-	/2026			-
				-
				-
Deed-	/2026			-
				-
				-
TOTAL =			83.4747	50.5907